


SYNERGIC SPACES

SYMPOSIUM AND ACCOMMODATION IN THE GREAT PLAIN

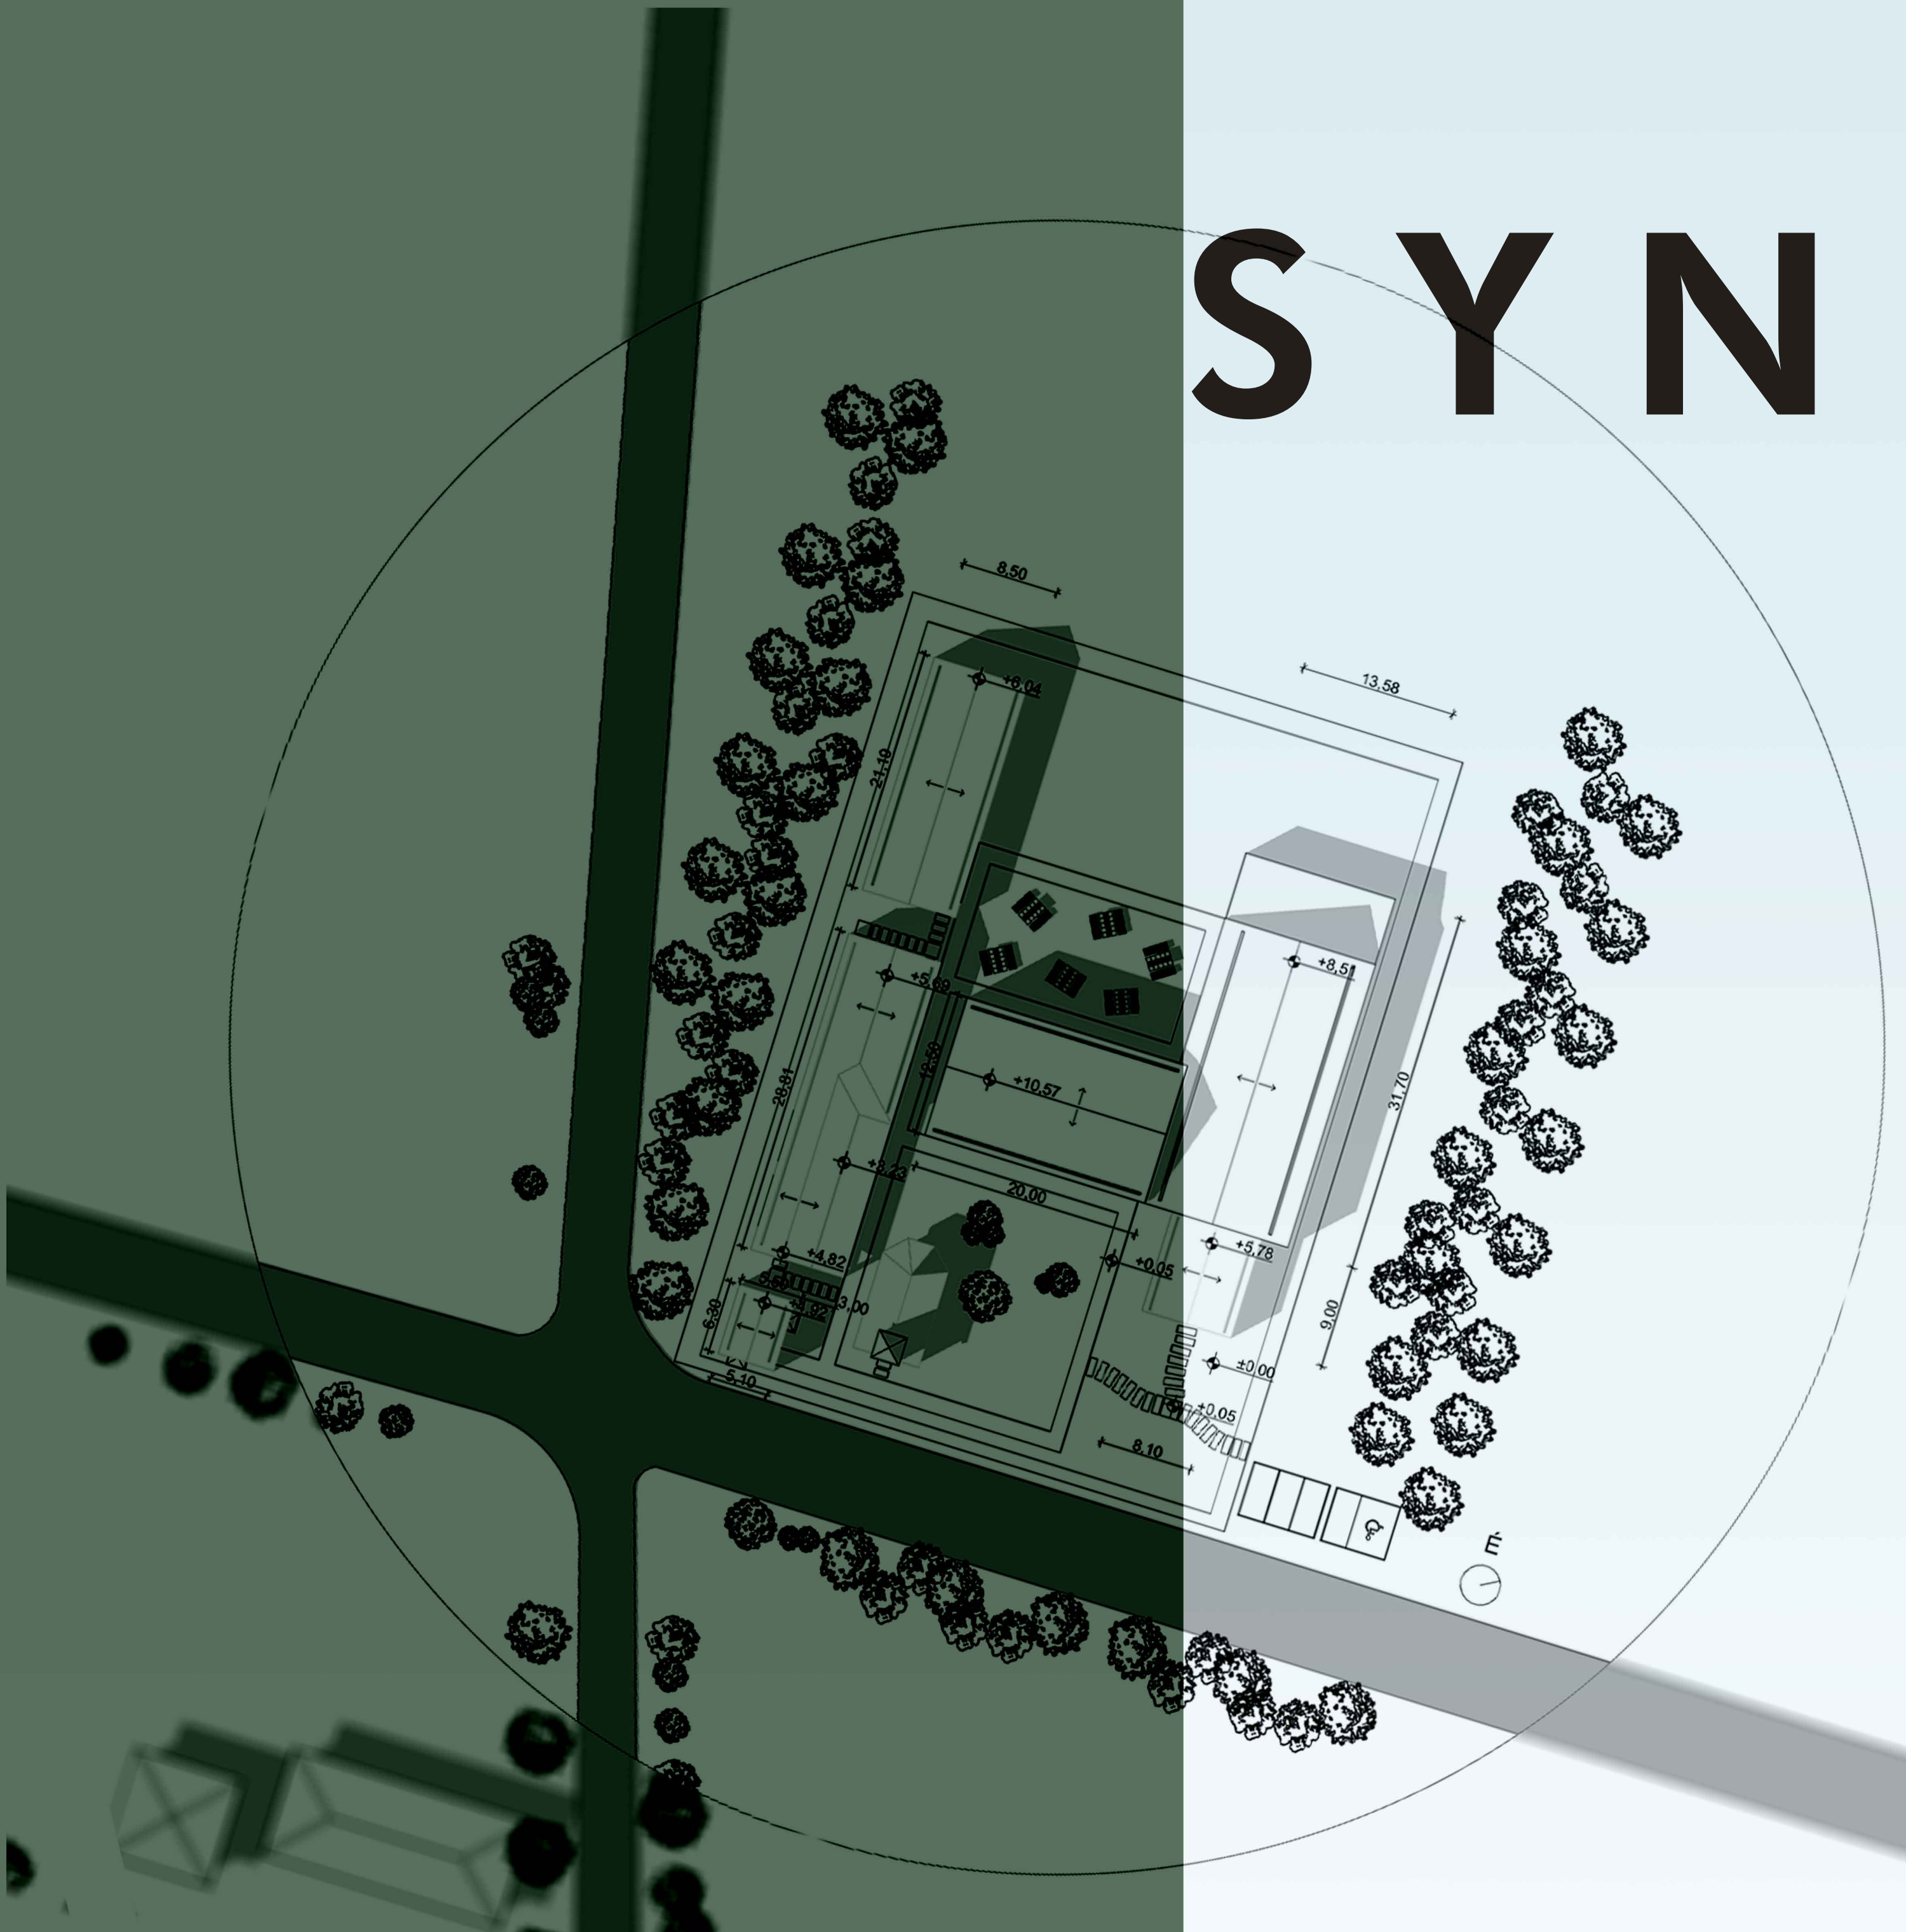

Az épületegyüttes a hagyományos alföldi karakter és a modern térszervezés dialógusa. A terv a zárt, védett vidéki gazdasági udvarok logikáját követi. A hagyományos csűrök archetipusából merítő, tiszta horizontális struktúrák tiszteletben tartják a táj léptékét, miközben intim belső udvart biztosítanak a kutatók és vendégek számára.

A komplexum a reprezentatív közösségi, az alkotó és a privát zónák tudatos ritmusára épül. Központi eleme a szimpóziumcsarnok, amely egyetlen hatalmas, 14 méter fesztávolságú, flexibilis tér. Karakterét a monumentális, látszó fa tetőszerkezet és a masszív oszlopsorok határozzák meg. Ezzel egyenrangú minőségben kapcsolódik hozzá a fogadóépület, az elcsendesedést biztosító szállásblokkok (accommodation volumes), valamint az informális együttlétnek helyet adó közösségi konyha és a gyakorlati alkotómunkát befogadó műhely (workshop), amelyek belső elrendezésükben pontosan igazodnak a specifikus funkcionális igényekhez.

Az anyaghasználat a tectonikus tisztaságra és a kontrasztokra épít. Az épületek külső burka egy monolitikus, patinás bontott téglá köpenyfal, amely összeköti a komplexumot a táj történelmi rétegeivel. Ezzel szemben a belső terekben a nyers textúra minden funkcionális egységben minimalista fehér vakolattá szelődül. Ez a semleges háttér felerősíti a természetes fényt, kiemeli a fa struktúra melegségét, és a csarnoktól kezdve a szállásokon át a műhelyig megteremti az alkotómunkához szükséges csendes atmoszférát.

