

SZONDI UTCA 60.

ÉPÜLETTERVEZÉS IV.

2024/2025/4.

FÜZET

NÉMETH ANNA

Környezet analízis

- Helyszín: Budapest Szondi utca 60.
- 6. kerület, Terézváros
- Legforgalmasabb, legélettelibb
- Kulturális központok - történelmi épületek központja



Környezet

- Viszonylag kevés zöldterület, néhány park zöldfelület
- Városliget - Jókai tér, Teréz körúti zöldfelületek
- Utcák mentén zöld növényzet és fák
- A sűrű beépítettség miatt nem sok



JÓKAI TÉR



HUNYADI TÉR

Közlekedés

- Közlekedési szempontból jól megközelíthető
- Közlekedési lehetőségei kiemelekedőek mind tömegközlekedés, mind az autós közlekedés
- M3-as metró nyugati téri megállója
- M1-es metró Bazsa utcai megállója
- 4-es, 6-os villamos Teréz körúton
- Számos busz, trolis: közvetlenül a 72-es trolis
- bicikliút
- Nyugati pályaudvar a közelben



Előnyök

- Kiváló eéhelyezkedés: közvetlen közel a Nyugati tér, Oktogon, Váci út, a Városliget
- Jó a közlekedés
- Kiváló infrastruktúra
 - Számos étterem, kávézók,
 - Kulturális intézmények (szépművészeti Múzeum)
 - Szabadidős programok
- Élénk városi élet
 - Bárok, étterem, üzletek (Westend bevásárlóközpont)
- Kórház a közelben
- Iskolák a közelben



Hátrány


- Ami előny az hátrány is lehet
- Magas forgalom és zajszennyezés
- Parkolási nehézségek
- Levegőszennyezés
- Kevés zöldterület
- Építkezés és felújítások zaja
- Túlzsúfoltság

Lehetőségek

- Szálláshelyek
- Üzleti lehetőségek: kereskedelmi egységek, kulturális vállalkozások
- Közlekedési és mobilitási fejlesztések
- Zöldterületek fejlesztése
- Kulturális és turizmus lehetőségek
- Társadalmi és közösségi lehetőségek

Funkció

- Főfunkció: sportközpont
 - Yoga/pilates studio –
- Mellékfunkció: cukrászda
 - Studio mellé egy minden mentes cukrászda

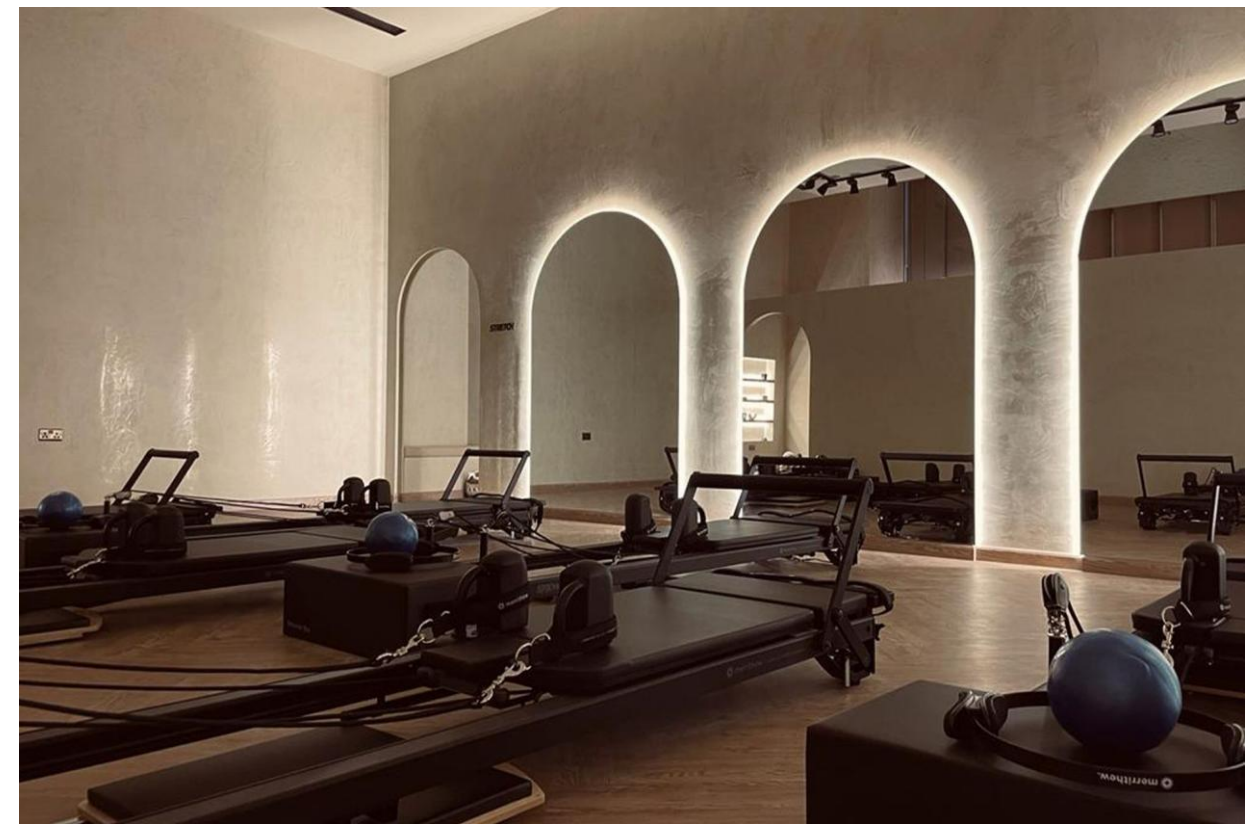

FORRÁS:

[HTTPS://HU.PINTEREST.COM/PIN/769200811340225422/](https://hu.pinterest.com/pin/769200811340225422/)

[HTTPS://HU.PINTEREST.COM/PIN/486177722291755066/](https://hu.pinterest.com/pin/486177722291755066/)

[HTTPS://HU.PINTEREST.COM/PIN/784259722648363345/](https://hu.pinterest.com/pin/784259722648363345/)

Helyszíni képek





Inspirációk - Pilates



FORRÁS:
[HTTPS://HU.PINTEREST.COM/PIN/23855073021983463/](https://hu.pinterest.com/pin/23855073021983463/)
[HTTPS://HU.PINTEREST.COM/PIN/9992430417914654/](https://hu.pinterest.com/pin/9992430417914654/)

Inspirációk - Jóga




FORRÁS:

[HTTPS://HU.PINTEREST.COM/PIN/956100195882727757/](https://hu.pinterest.com/pin/956100195882727757/)

[HTTPS://WWW.FAIRE.COM/PRODUCT/P_KFSPY7TYVV?SHOWIMAGEGALLERY=1&SHOWIMAGEGALLERYINDEX=0](https://www.faire.com/product/p_kfspy7tyvv?showImageGallery=1&showImageGalleryIndex=0)

Cukrászda inspiráció

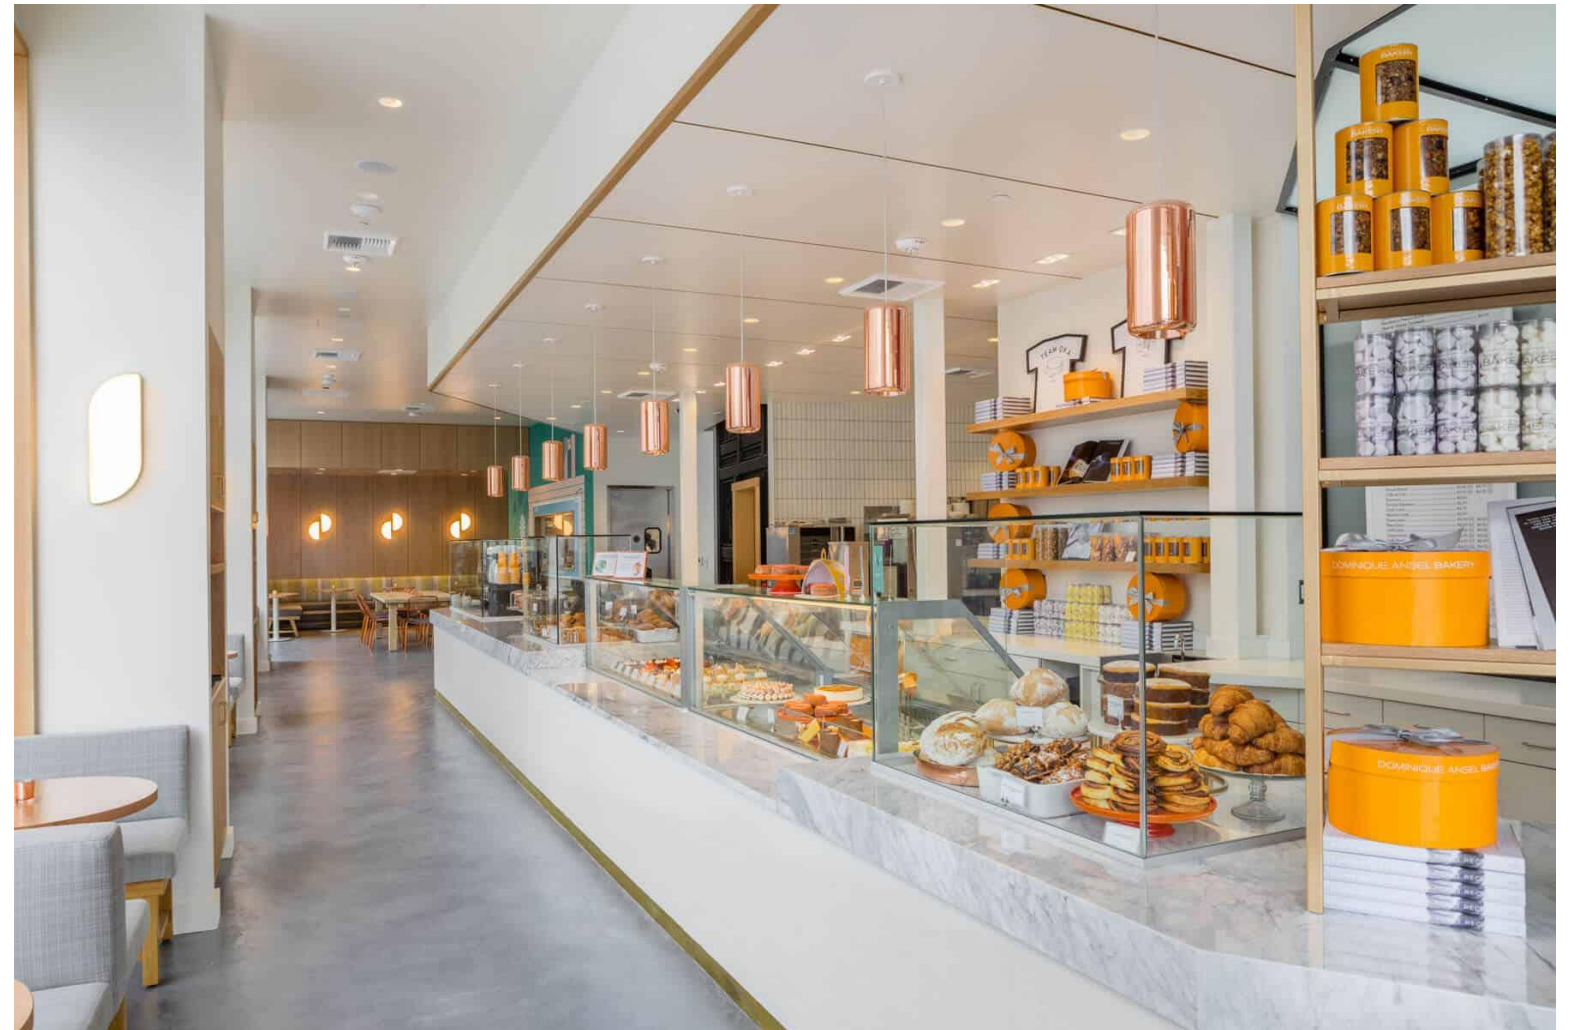


FORRÁS:

[HTTPS://ES.PINTEREST.COM/PIN/12384967722732270/](https://es.pinterest.com/pin/12384967722732270/)

[HTTPS://PASTRYARTSMAG.COM/PEOPLE/INSIDE-THE-MIND-OF-DOMINIQUE-ANSEL/](https://pastryartsmag.com/people/inside-the-mind-of-dominique-ansel/)

Cukrászda inspiráció

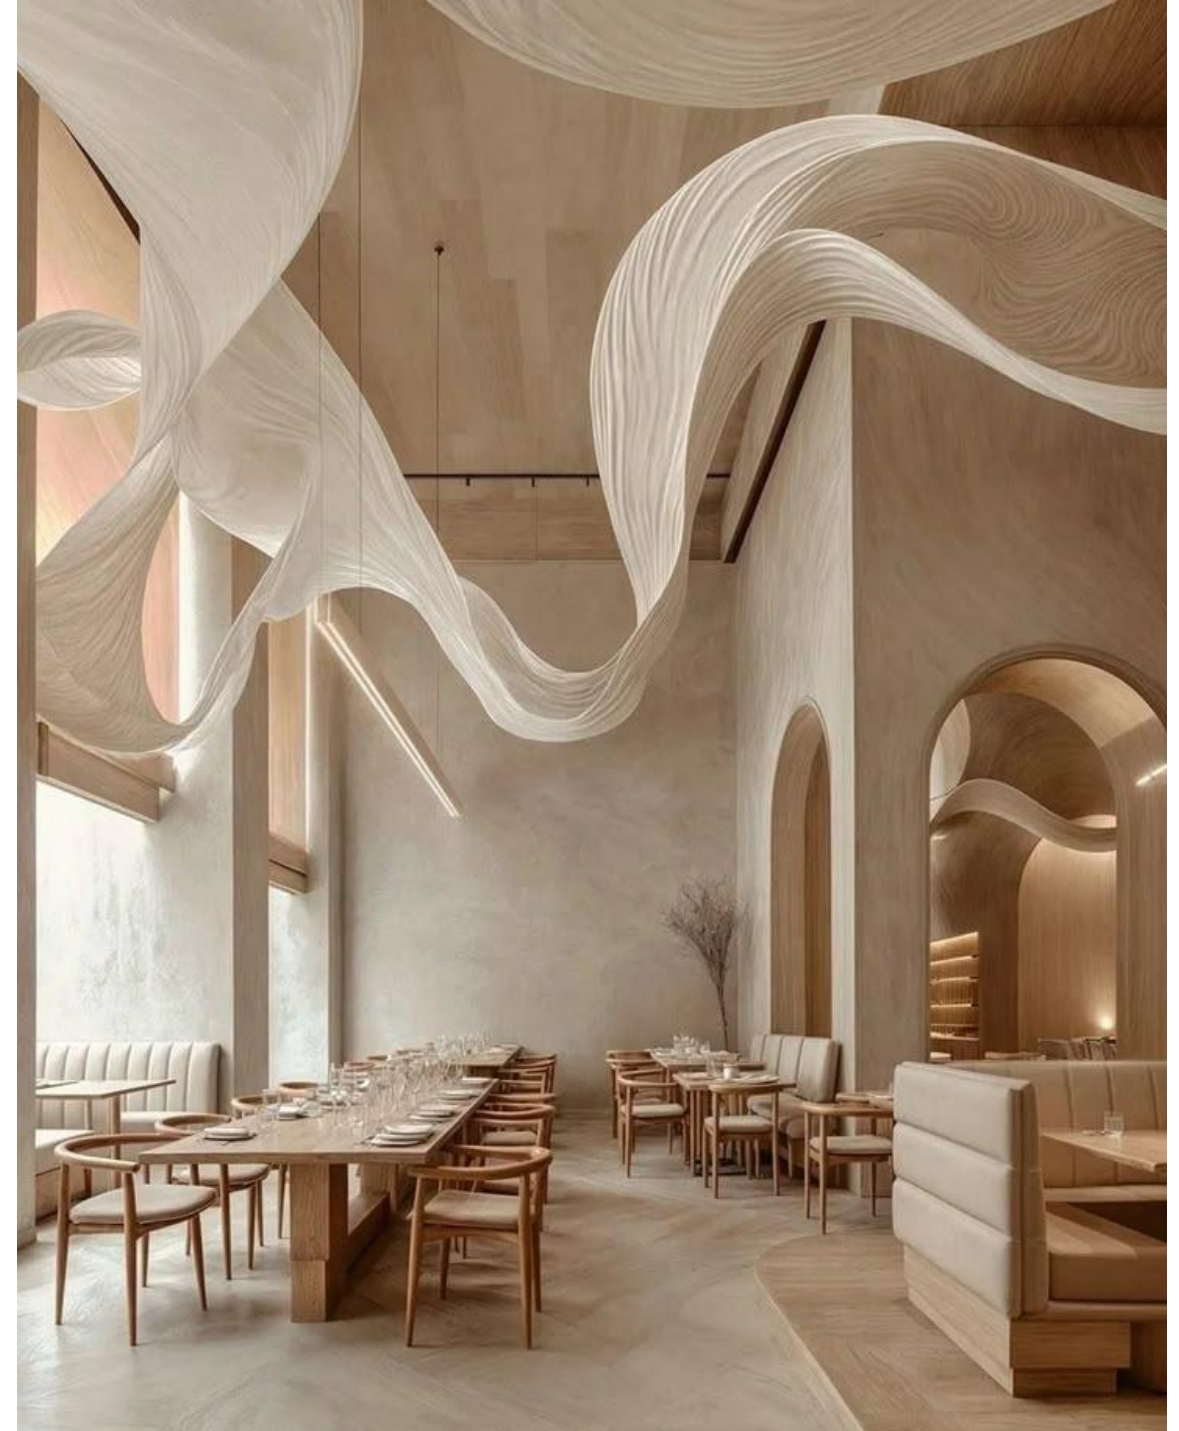

FORRÁS:


[HTTPS://HU.PINTEREST.COM/PIN/628041110575764851/](https://hu.pinterest.com/pin/628041110575764851/)

[HTTPS://2ENESTUDIO.COM/PRODUCTS/AUREA-ARENA-LAMPARA-COLGANTE-DE-OJO-DE-PERDIZ-Y-TERCIOPELO-COPIA-1](https://2enestudio.com/products/aurea-arena-lampara-colgante-de-ojo-de-perdiz-y-terciopele-cofia-1)

Tervdokumentáció


Helszínrajz

$M=1:1000$

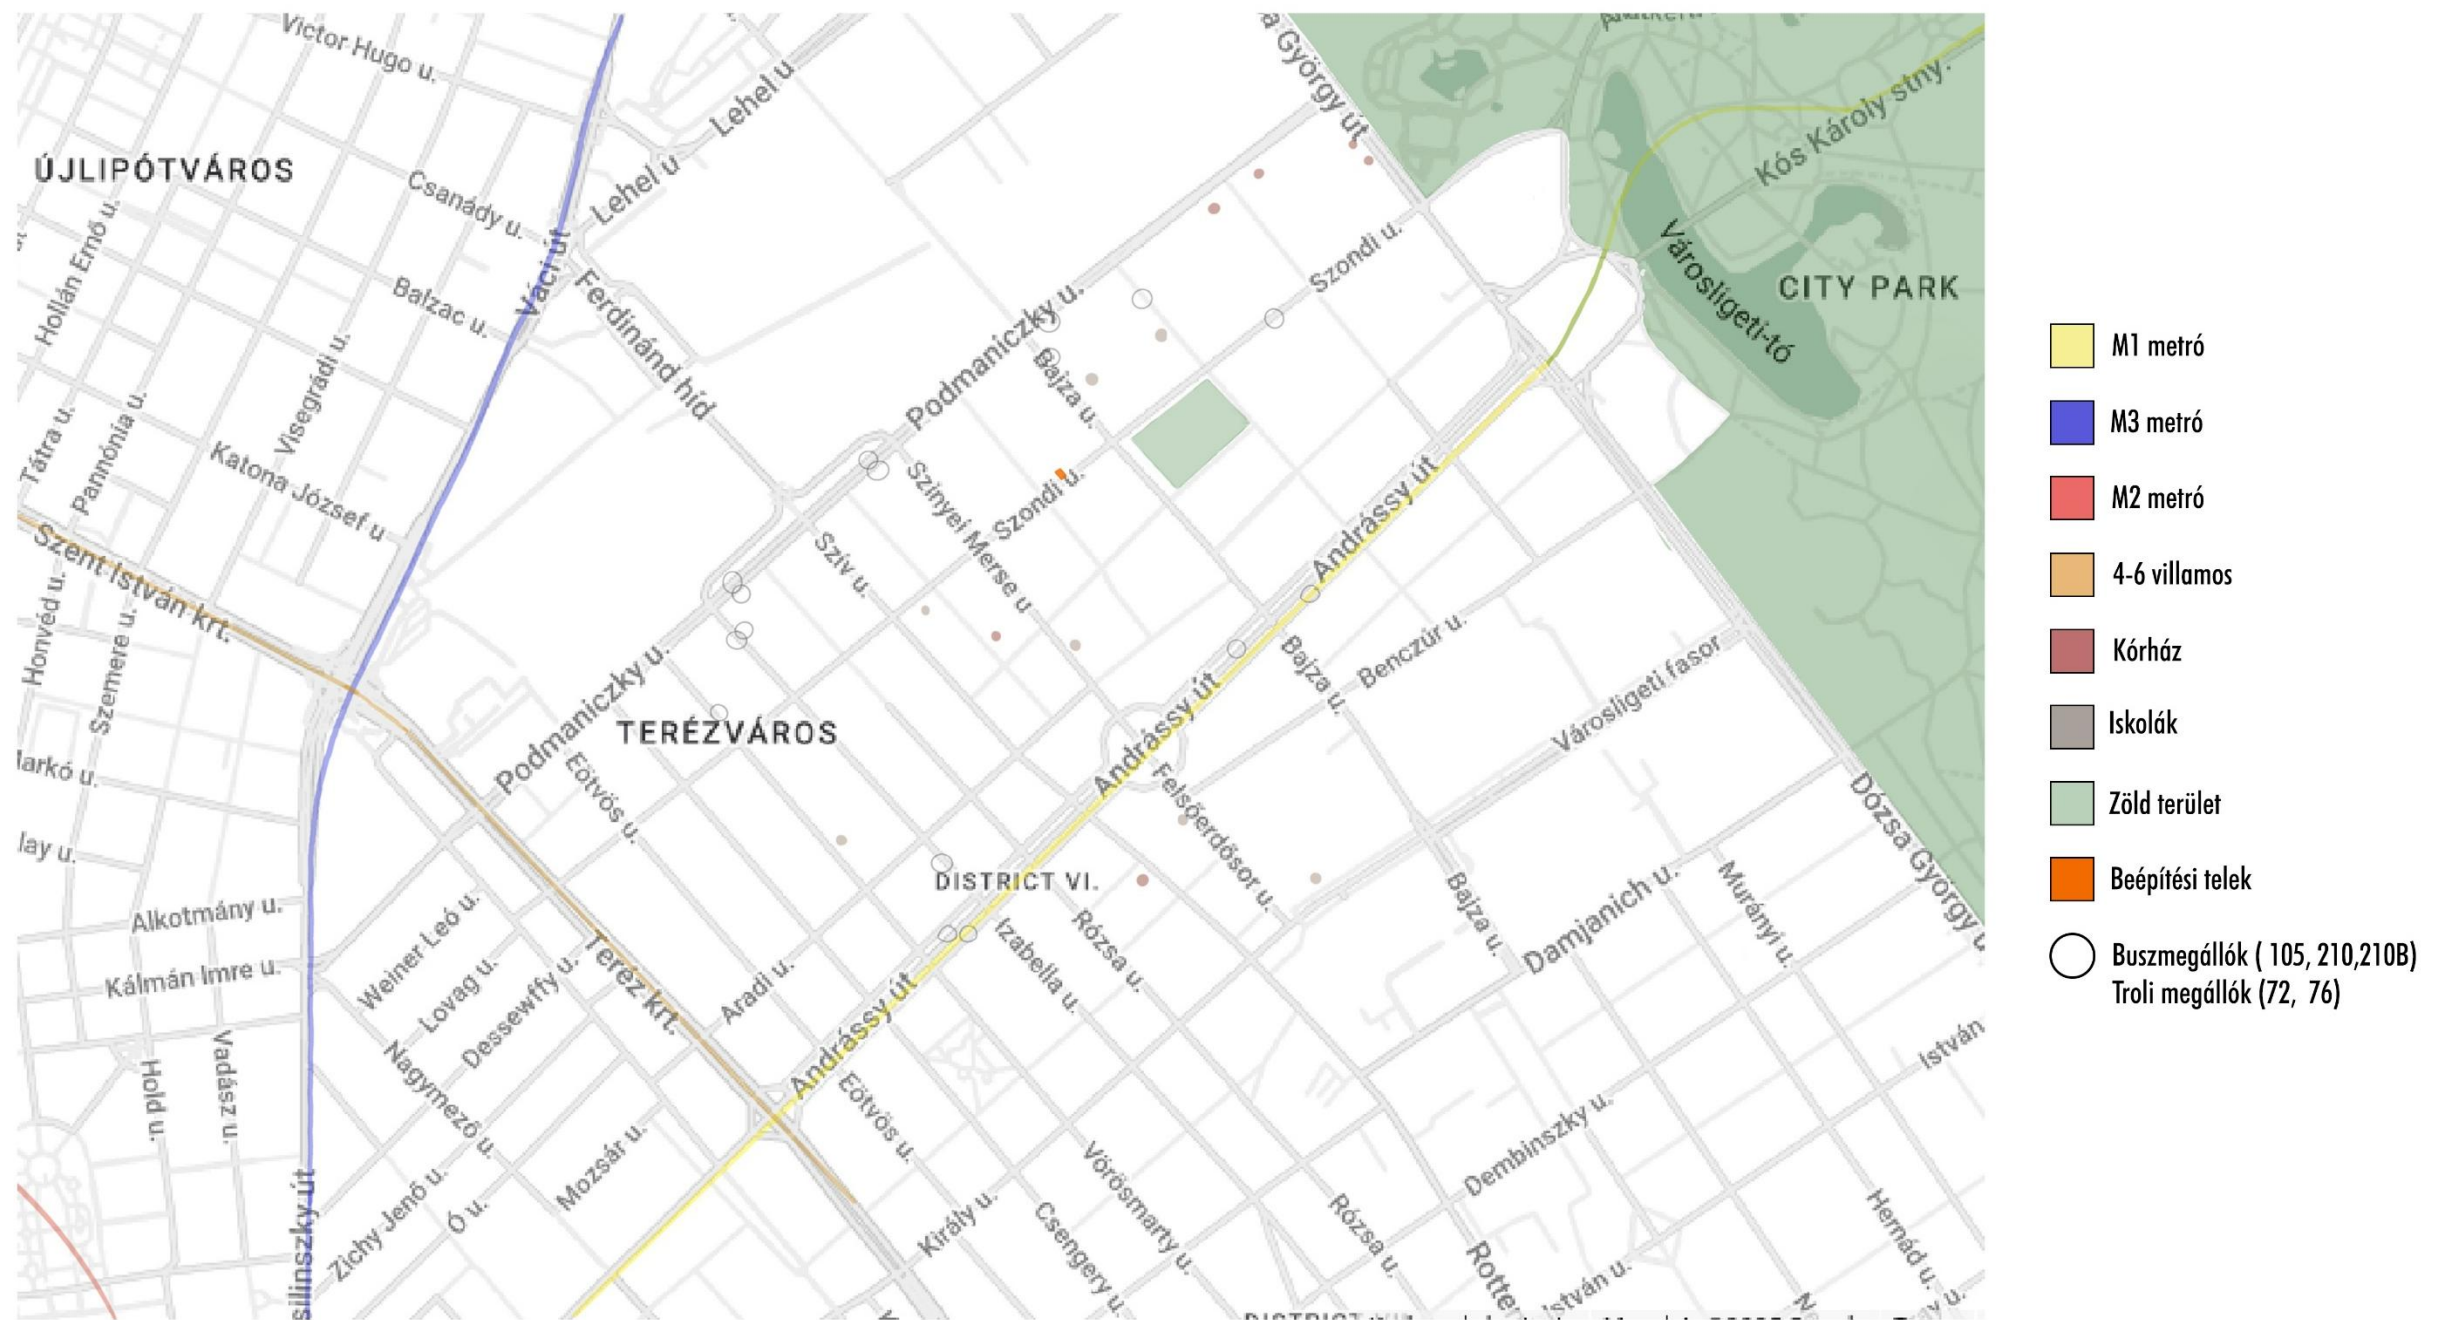

Helyszínrajz

M=1:200

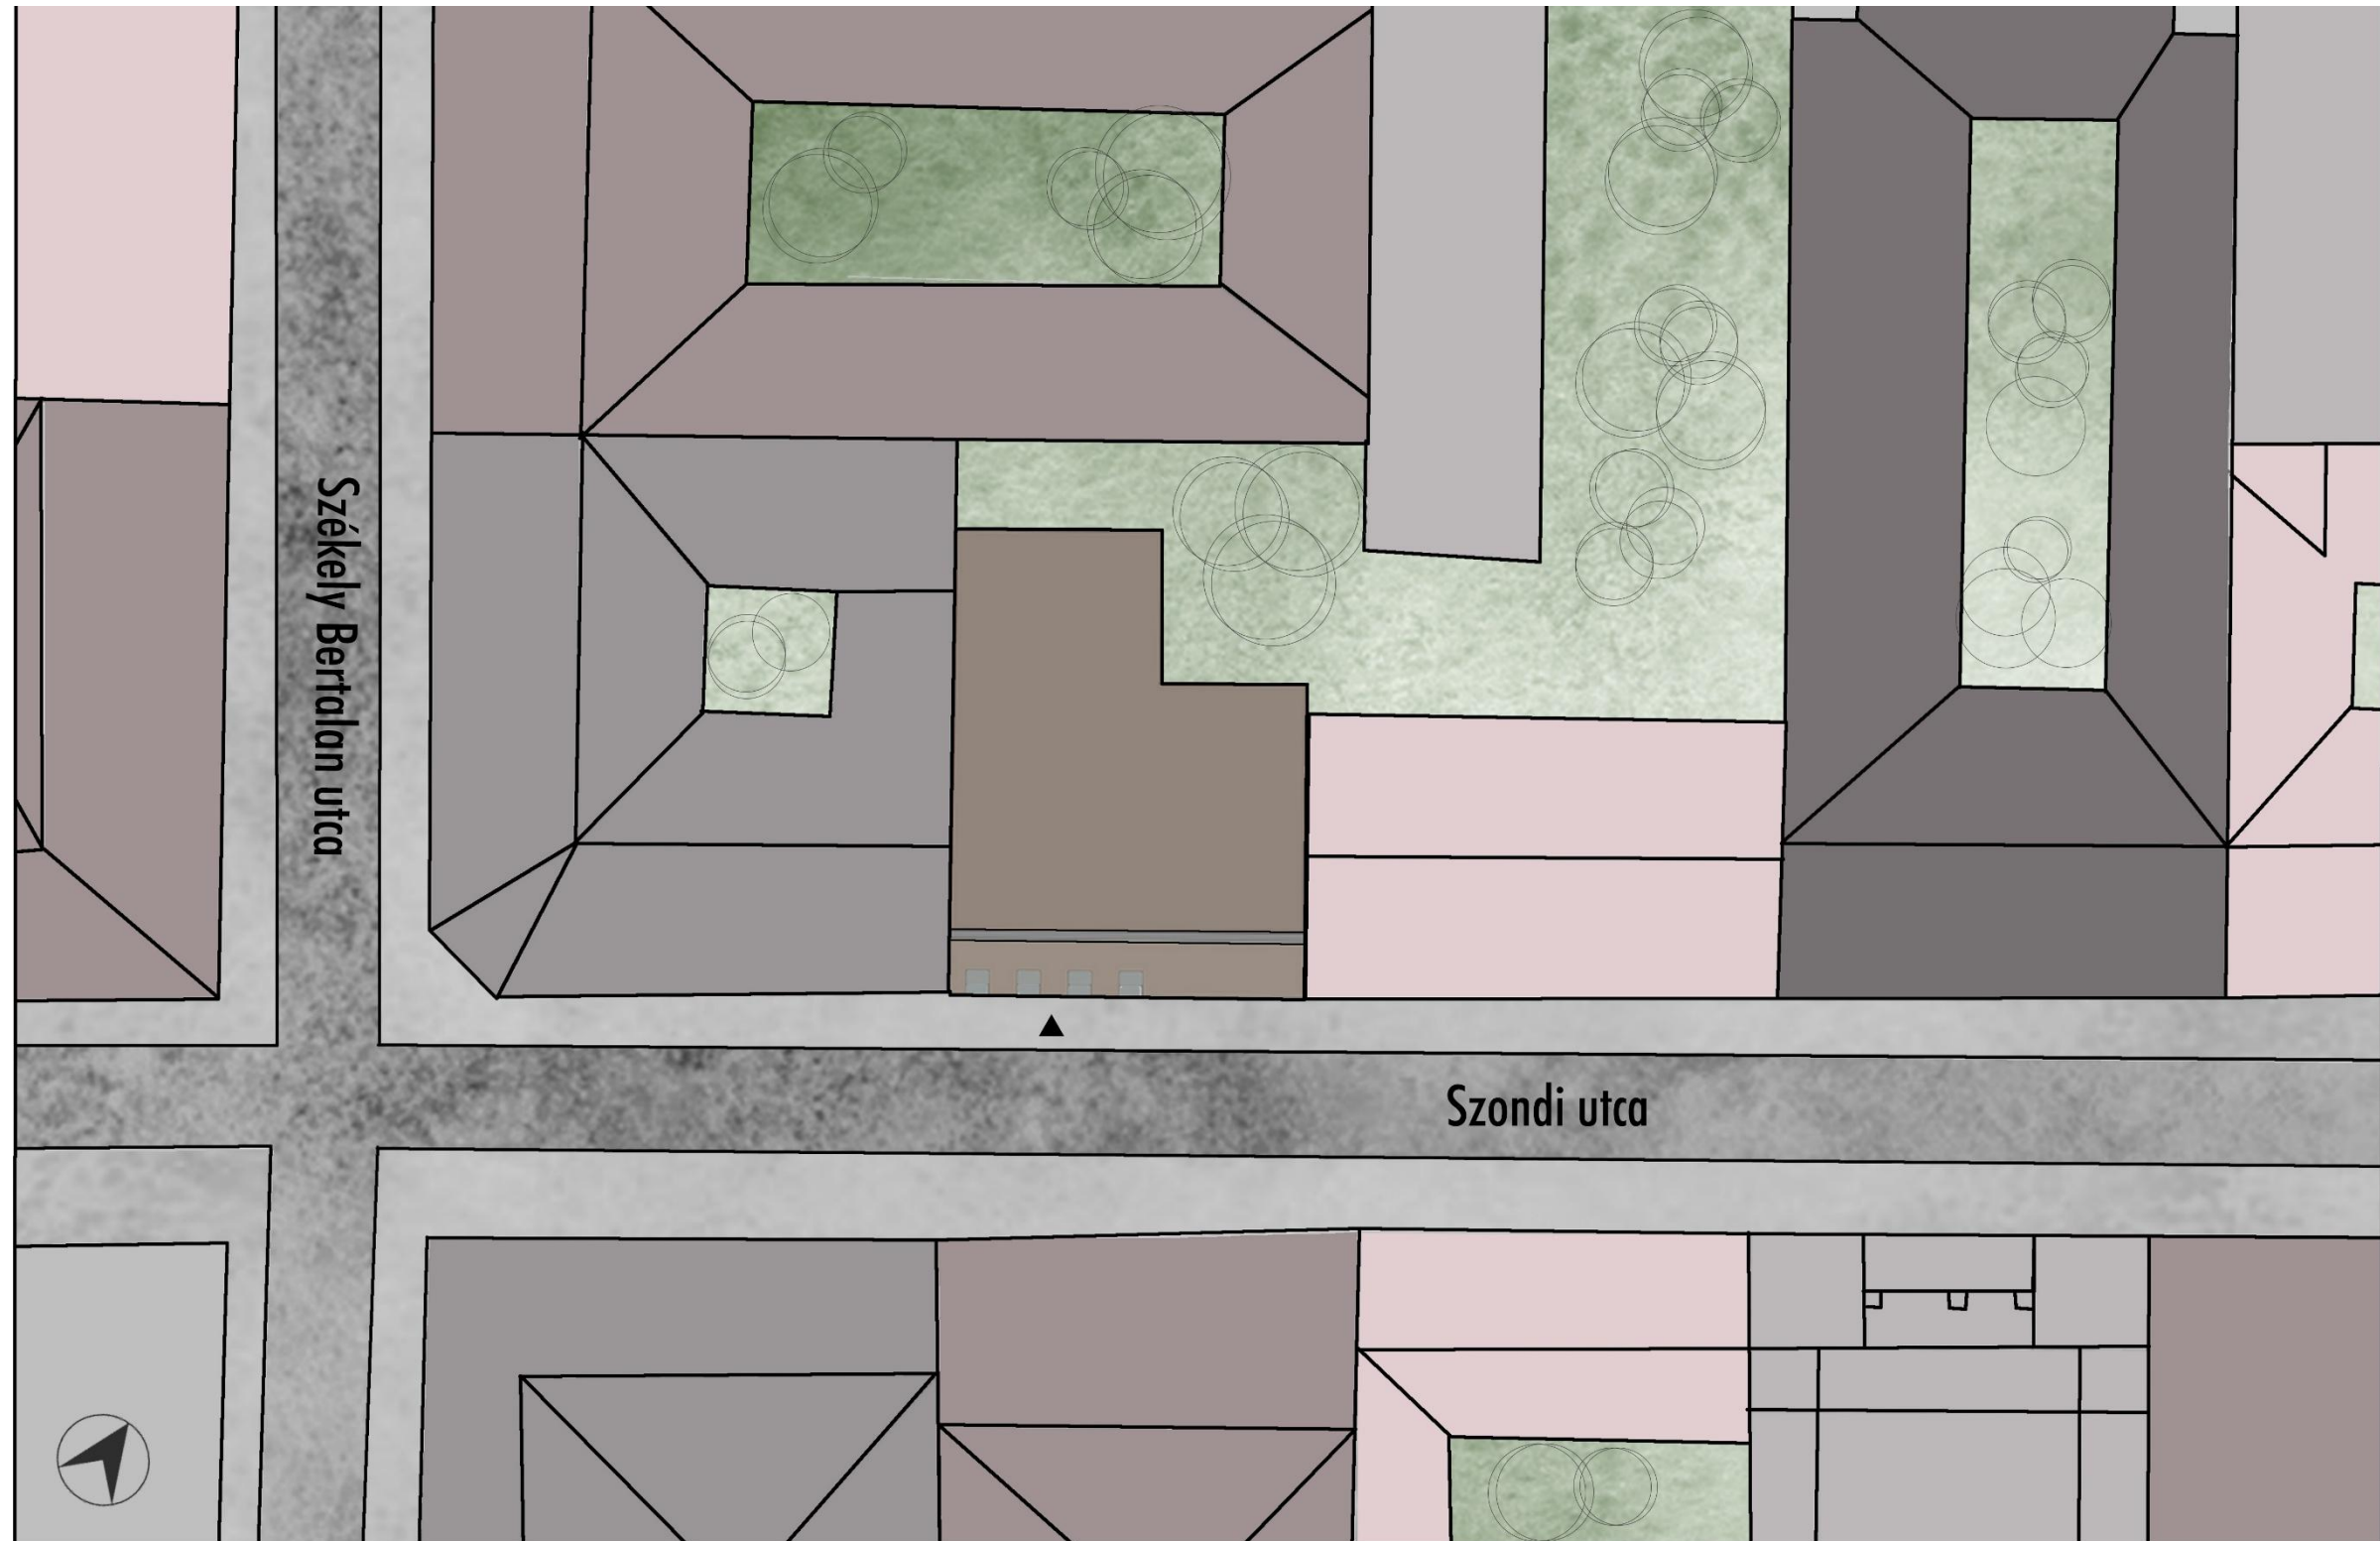

Alaprajz Földszint

M=1:100



Alaprajz 1.emelet

M=1:100



Alaprajz 2.emelet

M=1:100




Alaprajz 3.emelet

M=1:100



Alaprajz 4.emelet

M=1:100

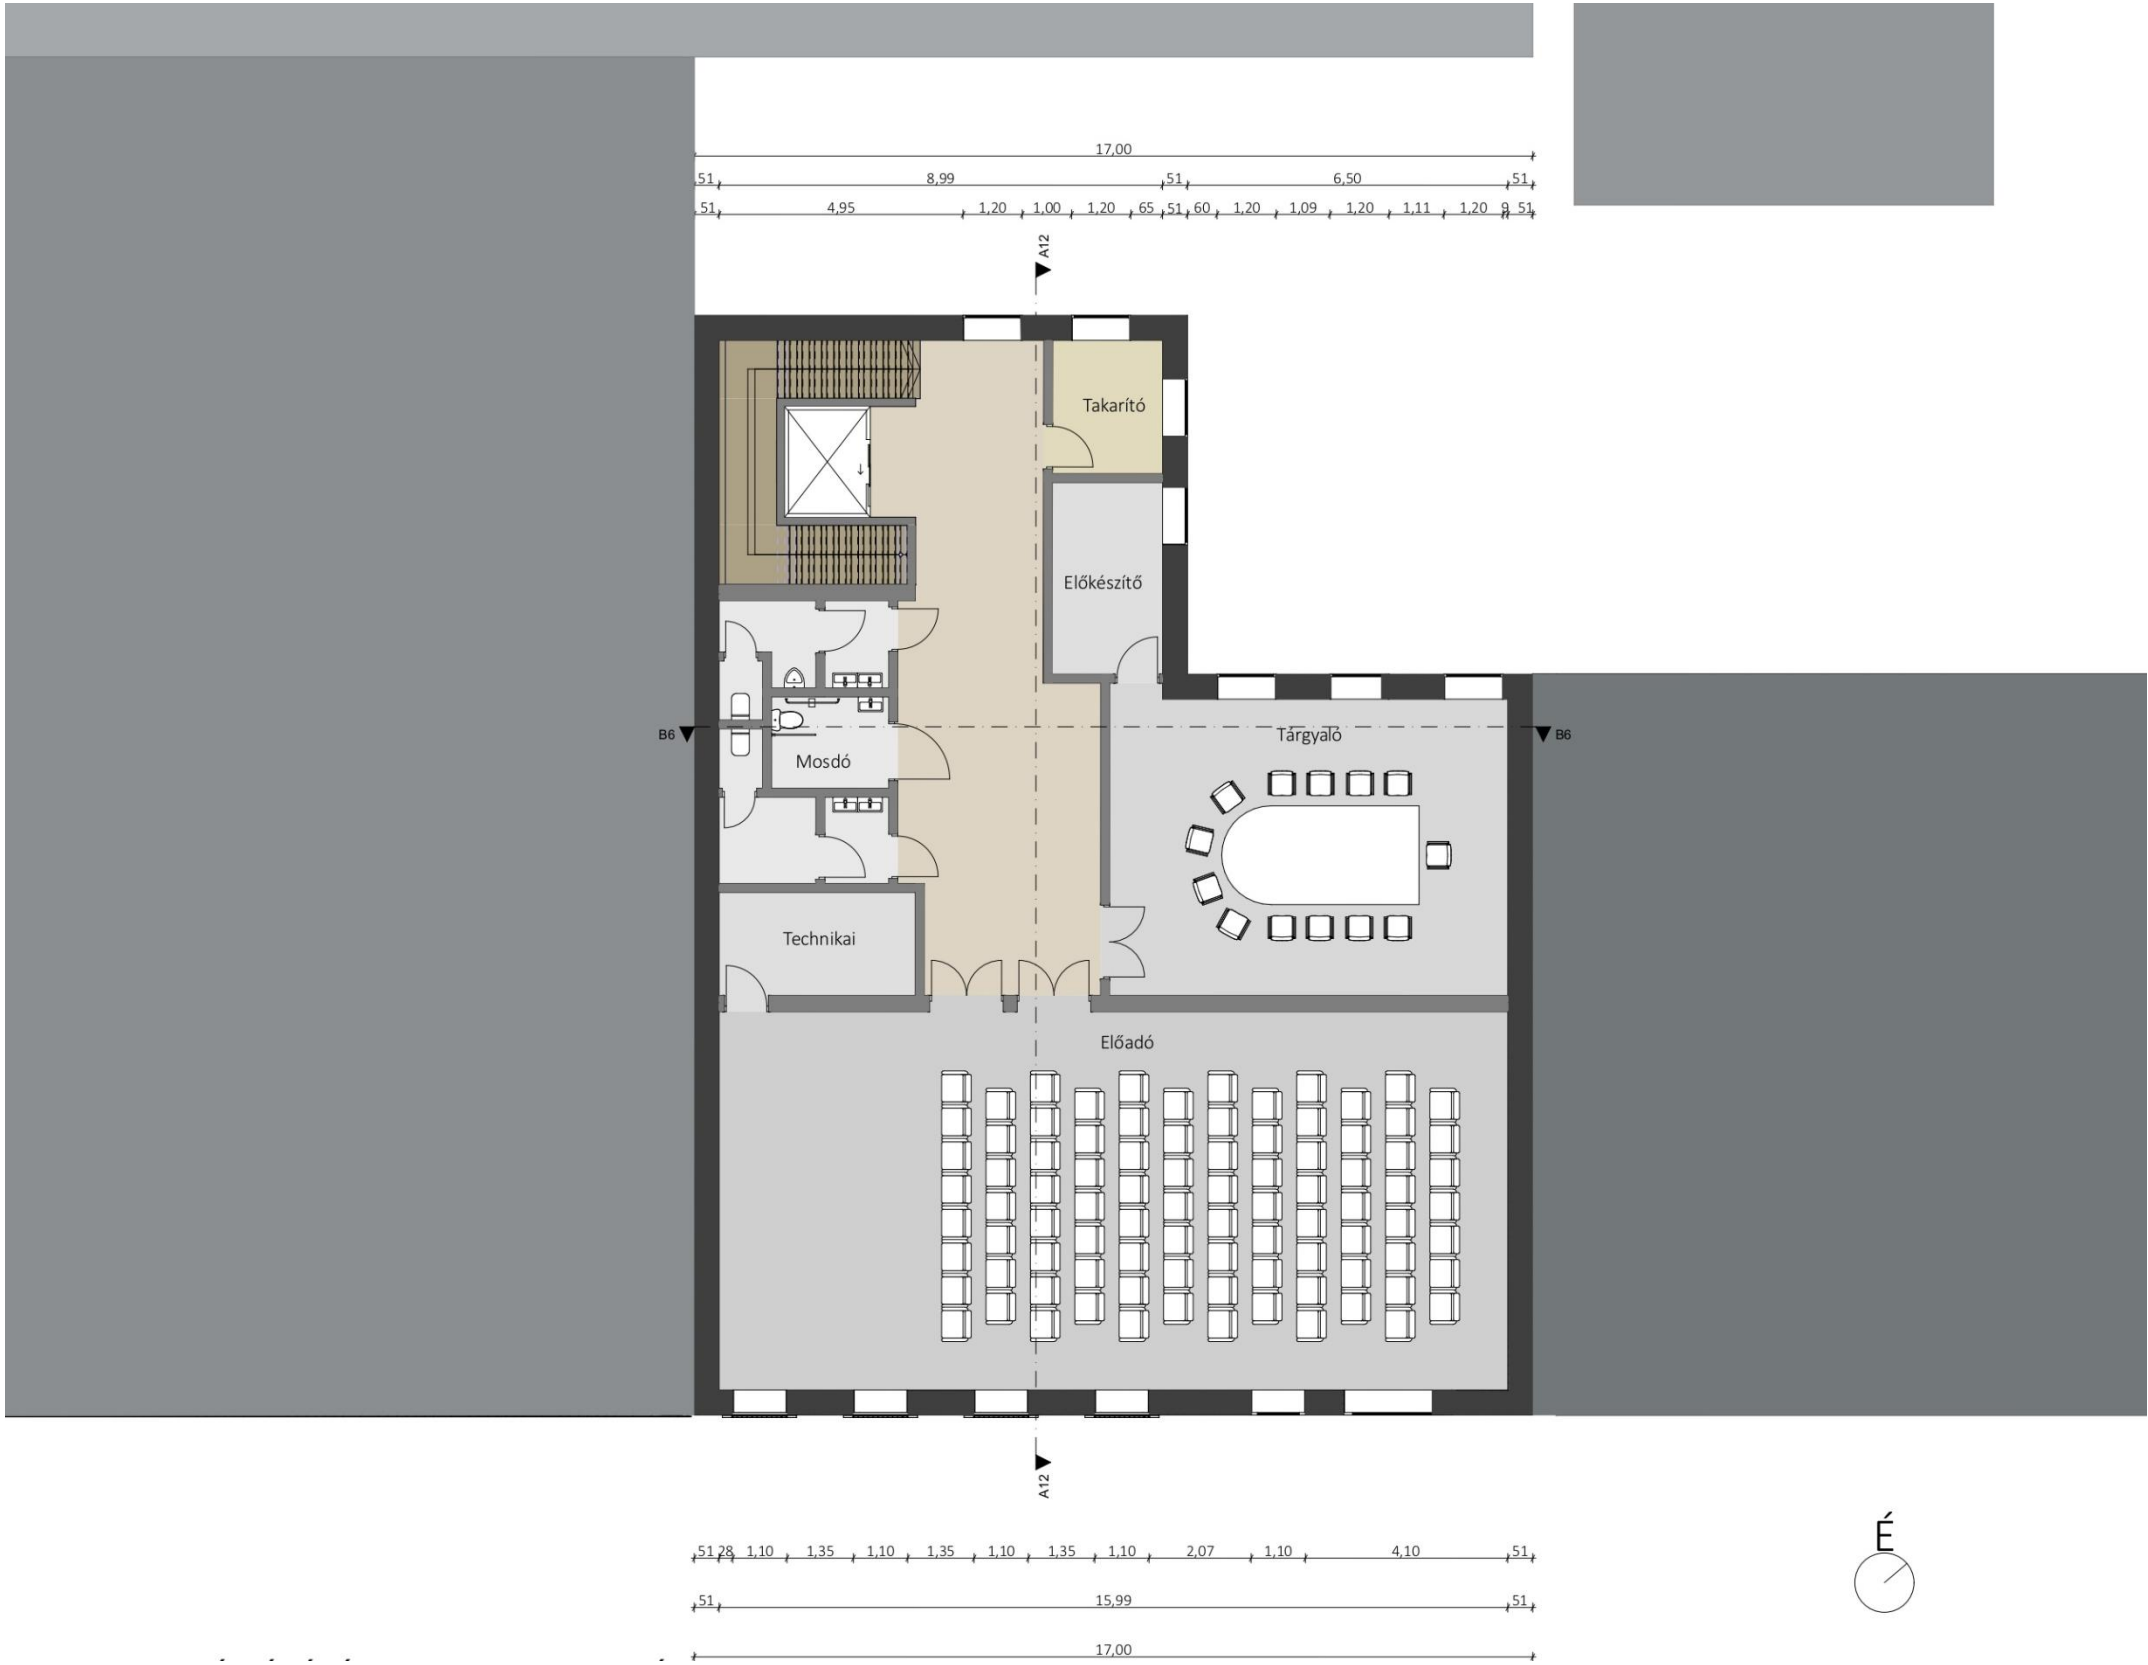

Metszet

M=1:100



Homlokzat


M=1:100



Látványterv



Látványterv - udvar

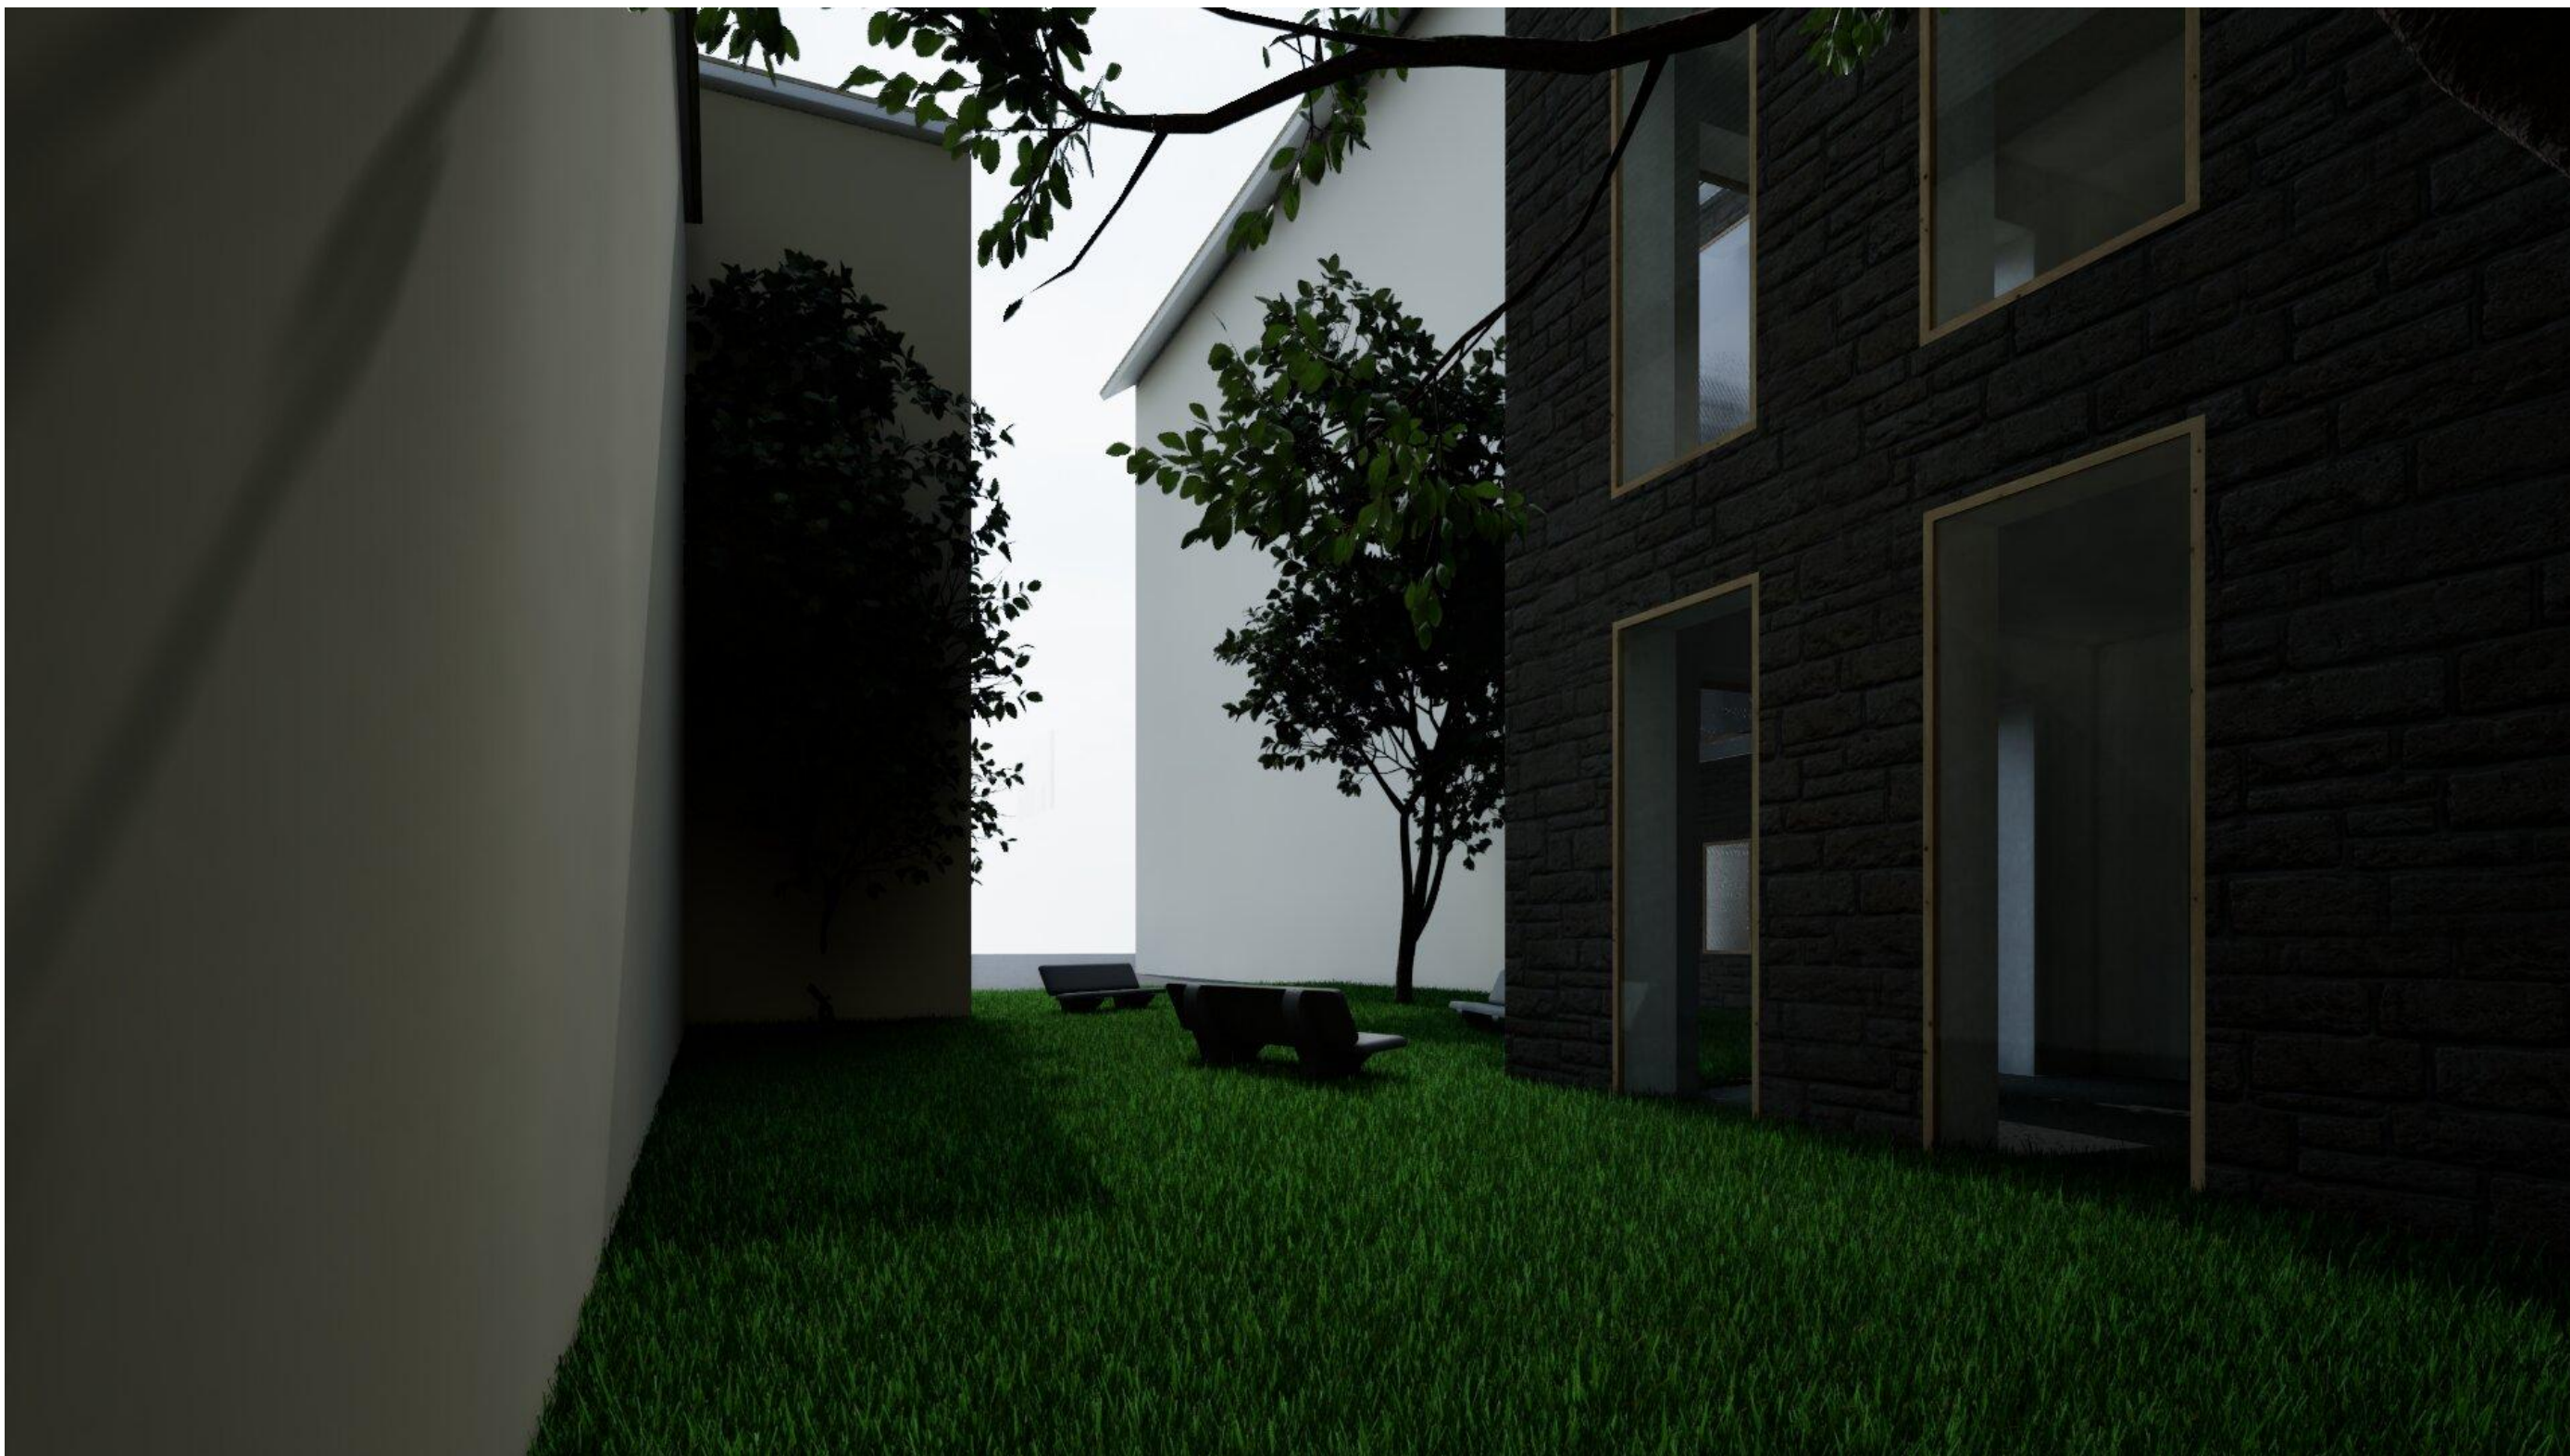

Látványterv



Látványterv



Látványterv



Makett fotók



Makett fotók



Makett fotók



Makett fotók



Makett fotók

